

ÇİZİM 3 — TOPRAKLAMA VE YILDIRIMDAN KORUNMA

A) KAT PLANI (üstten görünüş) — ölçek 1:150

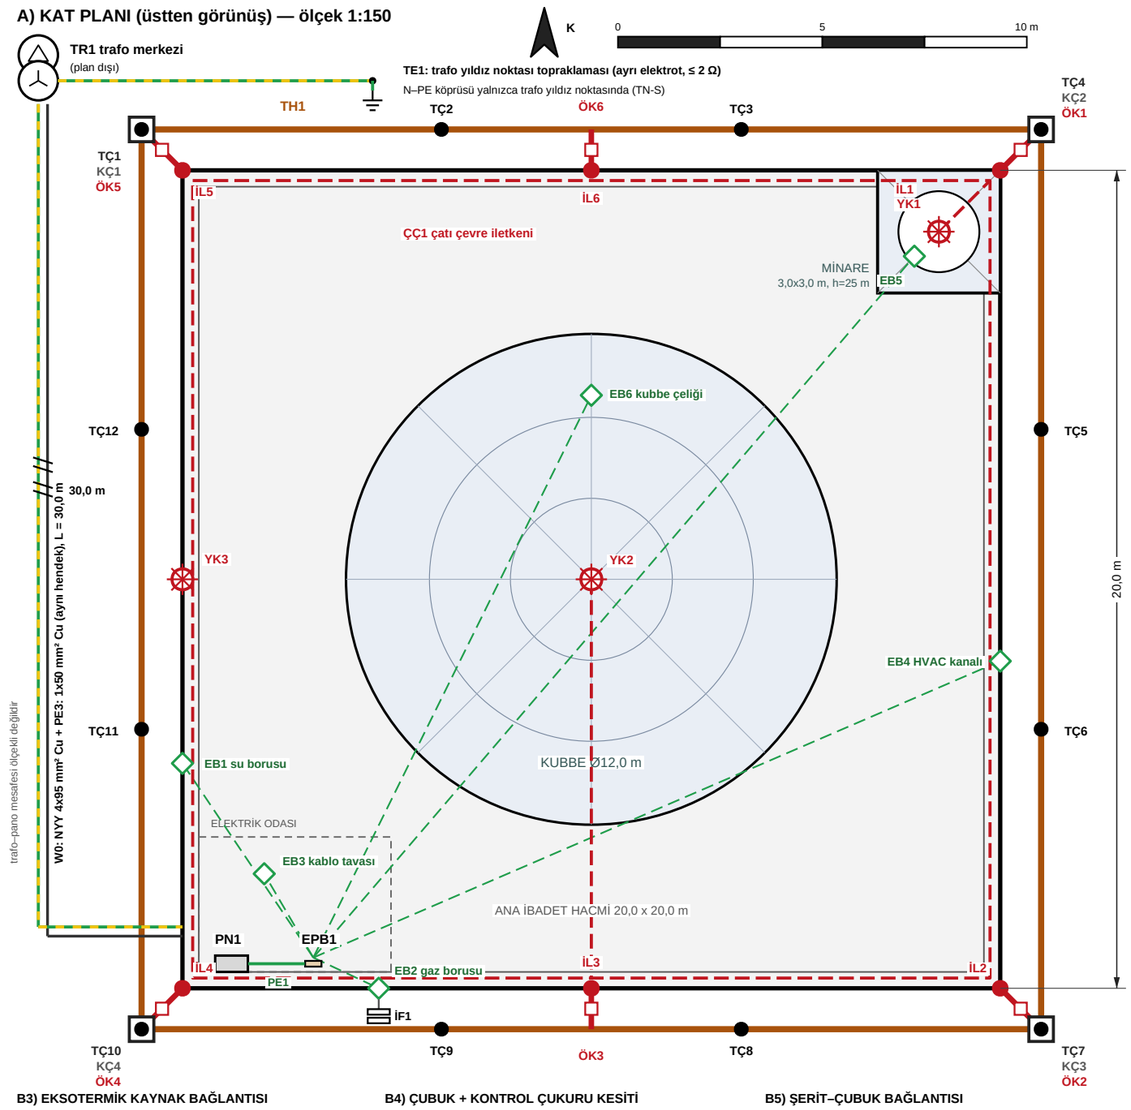


B) DETAY VE KESİTLER

B2) YUVARLANAN KÜRE YÖNTEMİ — koruma seviyesi III (R = 45 m) — 1:500

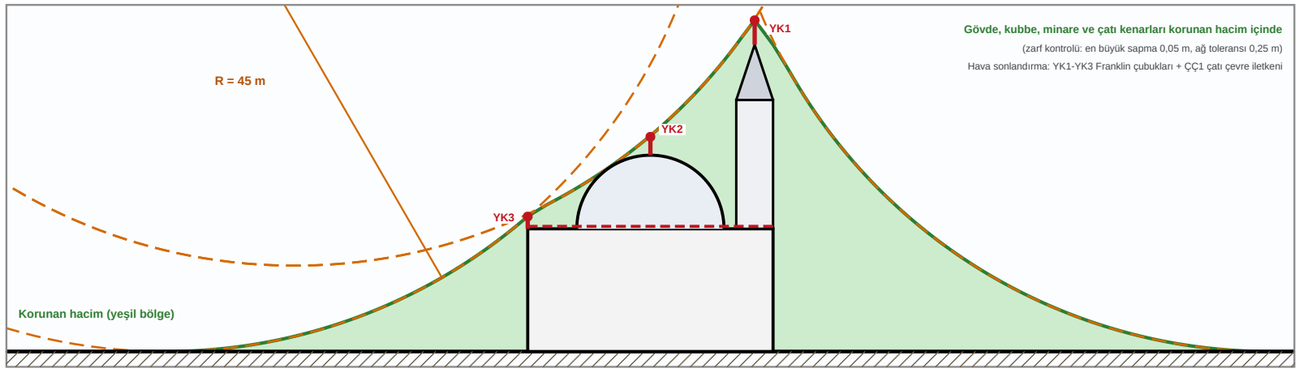


B1) BİNA KESİTİ (yan görünüş) — 1:200

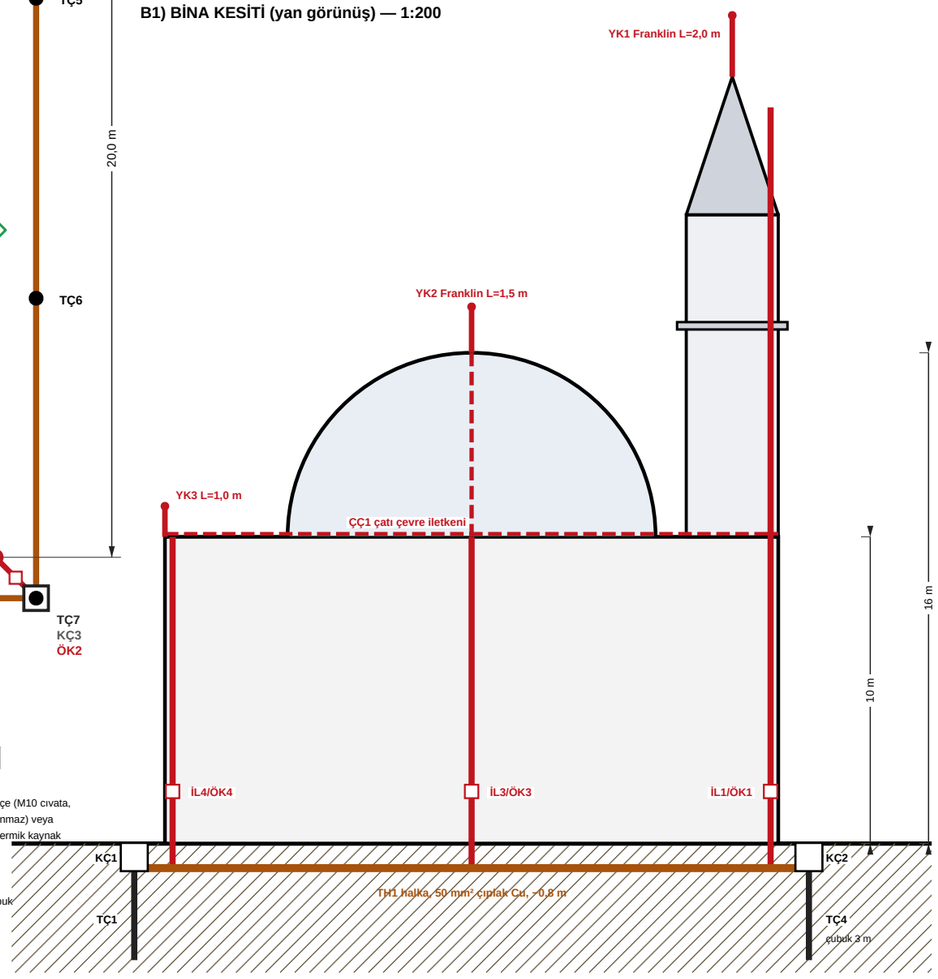

B6) EPB ŞEMASI


(hangi parçalar bağlanıyor)

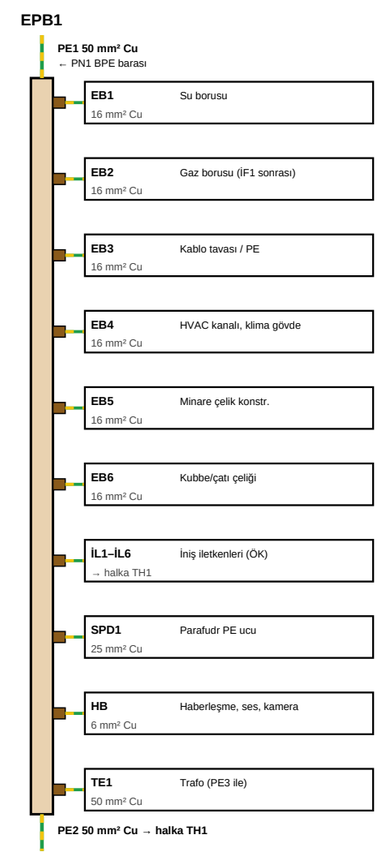

Tüm sistemler (güç, yıldırım, haberleşme) tek ortak topraklamaya bağlanır.

B3) EKSOTERMİK KAYNAK BAĞLANTISI


EK1 — şematik, ölçeksiz

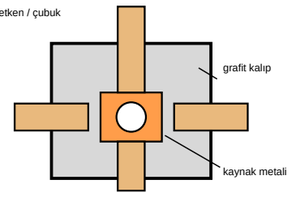

T bağlantı (şerit–çubuk, halka–iniş iletkeni)


B4) ÇUBUK + KONTROL ÇUKURU KESİTİ

TÇ / KÇ — şematik, ölçeksiz

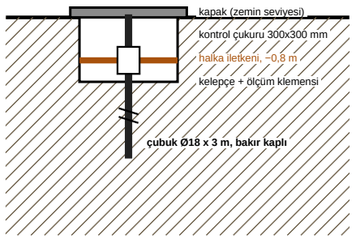

B5) ŞERİT–ÇUBUK BAĞLANTISI

şematik, ölçeksiz

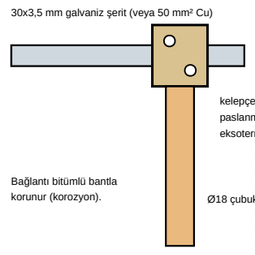

NOTLAR

1. Tüm sistemler (güç, yıldırım, haberleşme) tek ortak topraklamaya bağlanır; ölçüm hedefi ≤ 1–2 Ω, kuru mevsimde tekrar ölçülür.
2. Halka: bina çevresinde 1,0 m dışta, 0,8 m derinlikte 50 mm² çıplak Cu (≈ 88 m); 12 adet Ø18x3 m çubuk (aralık ≤ 7,3 m), 4 kontrol çukuru.
3. Yıldırım koruma seviyesi III (R = 45 m): 6 iniş iletkeni (ort. aralık 13,3 m ≤ 15 m), her biri ölçüm ayırma noktalı (ÖK) ve halkaya eksotermik kaynaklıdır.
4. Gaz borusunda izolasyon flanşı (İF1) kullanılır; su/gaz borusu, kablo tavası, HVAC kanalı ve çelik konstrüksiyon EPB1'e bağlanır.
5. TE1: trafo yıldız noktası için ayrı elektrot (≤ 2 Ω); PE3 ile PN1 BPE barasına bağlanır. N–PE köprüsü yalnız trafodadır.
6. Yeraltı bağlantıları eksotermik kaynaklıdır; ölçümler kontrol çukurlarından yapılır. Poz no'lar Çizim 1-2 ve tablolarla aynıdır.

GÖSTERİMLER

- TH1 halka (50 mm² çıplak Cu, −0,8 m)
- yıldırım iletkenleri (iniş, ÇÇ1)
- PE / eş potansiyel (EB)
- topraklama çubuğu
- kontrol çukuru
- ölçüm ayırma noktası
- eş pot. noktası

Cami Elektrik Dağıtım Projesi	**400 V TN-S**
ÇİZİM ADI: **TOPRAKLAMA VE YILDIRIMDAN KORUNMA**	
ÇİZİM NO: **CEP-E-03**	ÖLÇEK: **1:150 / 1:200 / 1:500**
TARİH: **24.10.2026**	REVİZYON: **R0**
SAYFA: **3/3**	
ÇİZEN: **proje_uret.py**	KONTROL: **Yetkili Elk. Müh. (onay bekliyor)**